
PLANTA BAJA — piers (muros de N 0.00 a N+3.00)

Color = un pier con su nombre · gris = muro sin pier (antepechos, dinteles, muretes) · cuadro negro = castillo

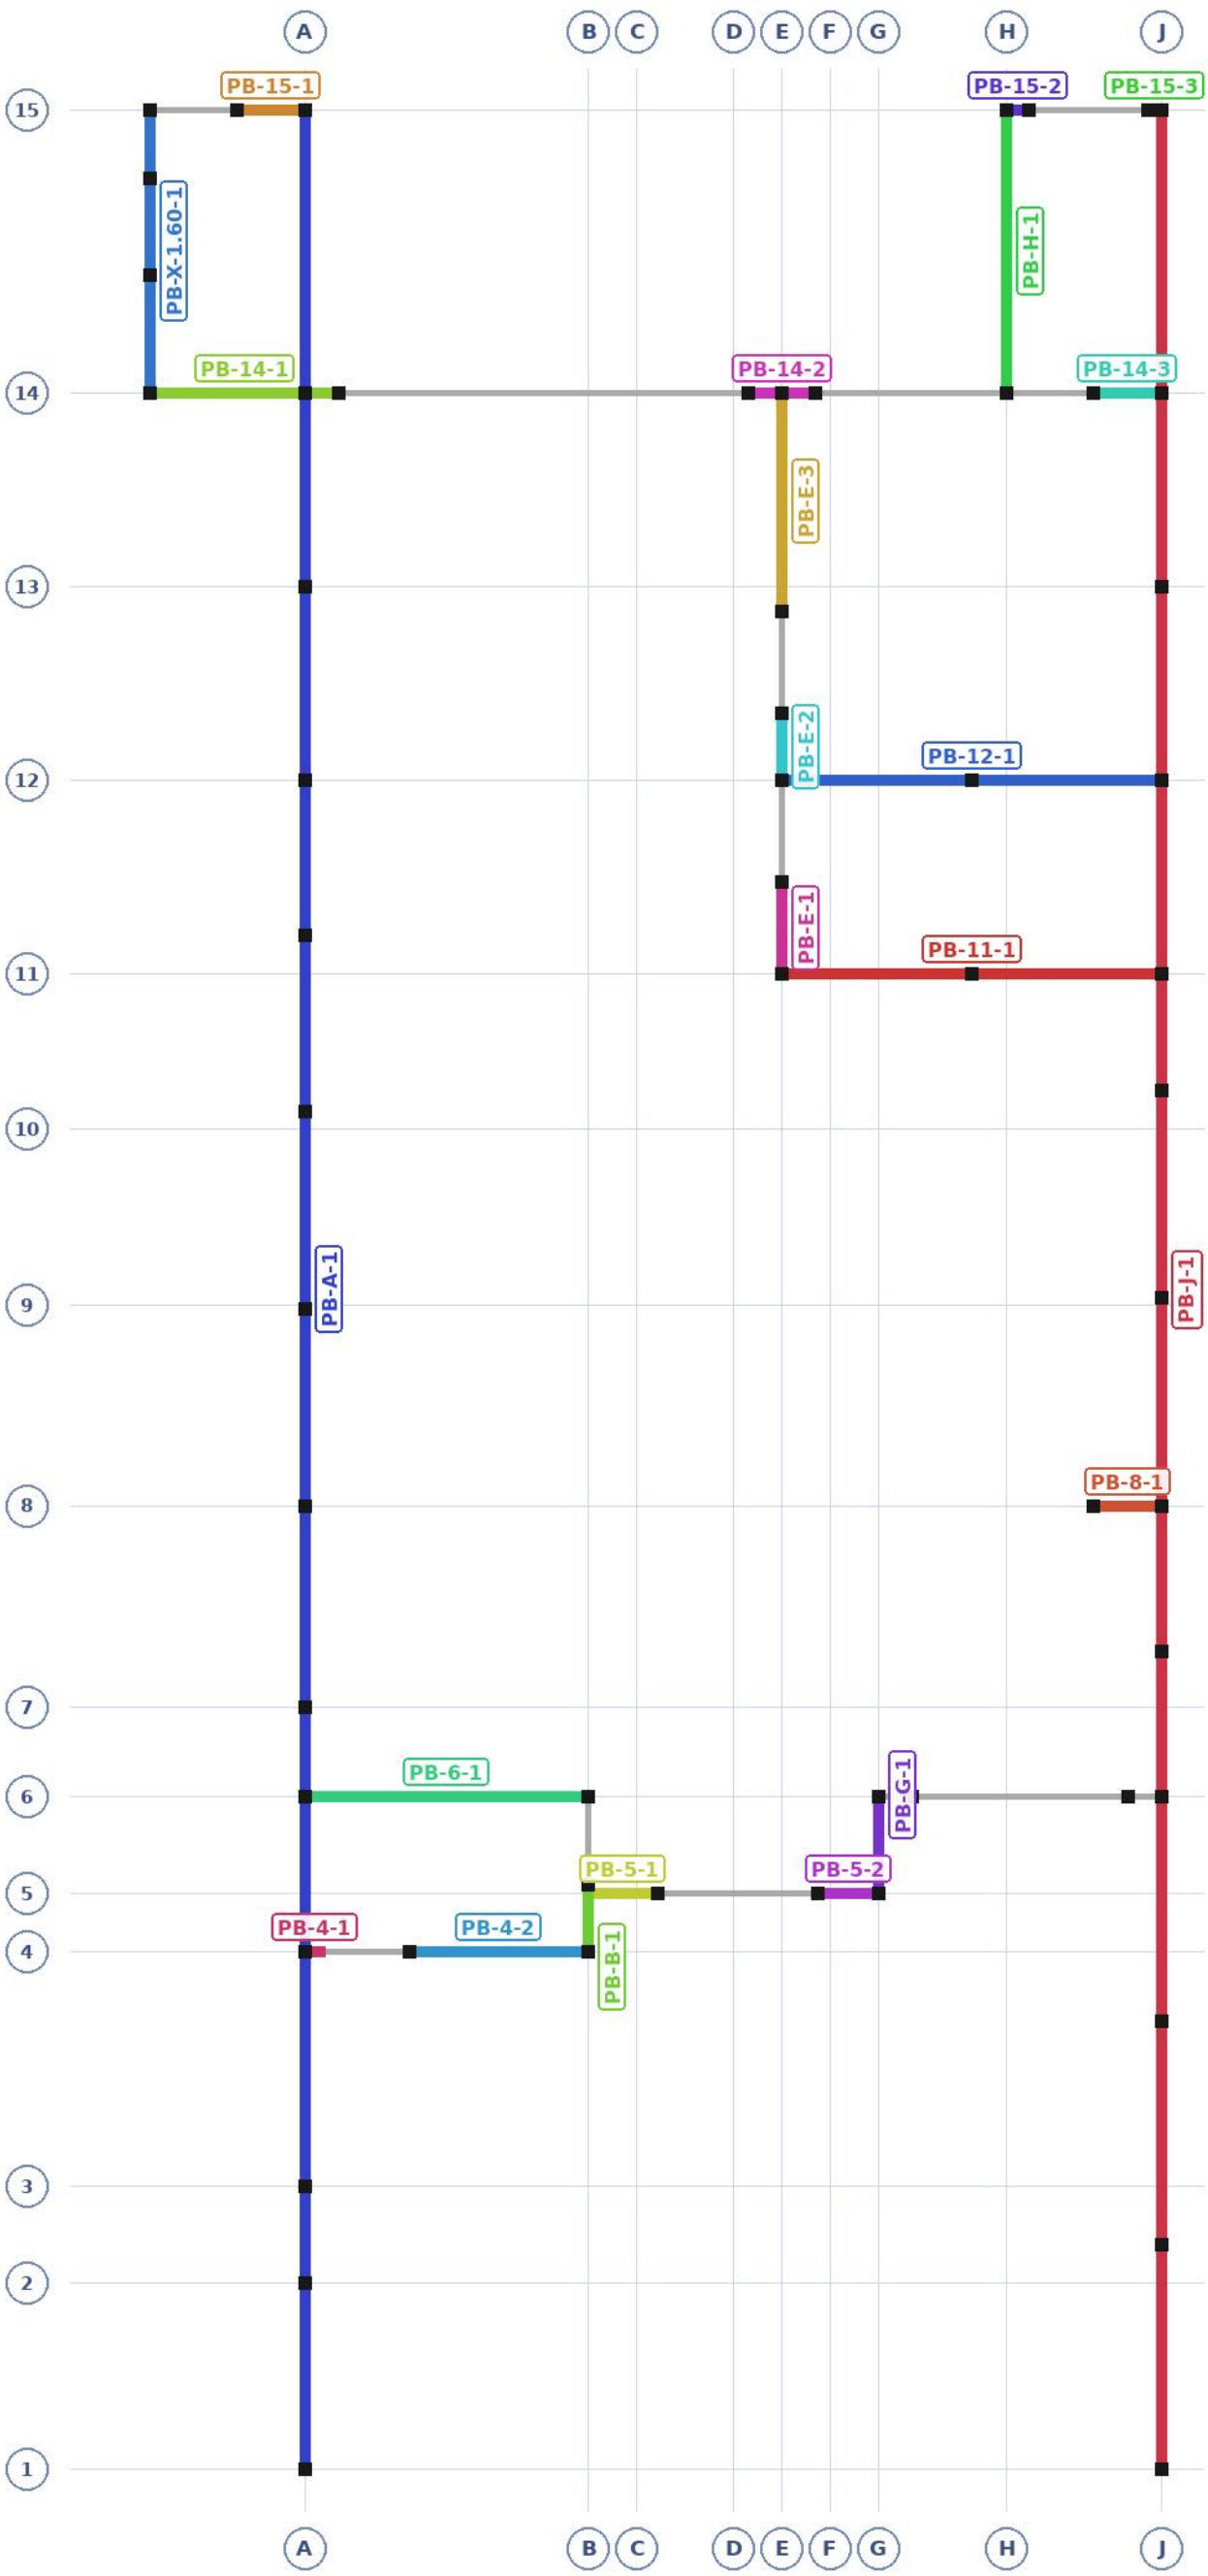

PLANTA ALTA — piers (muros de N+3.00 a N+6.00)

Color = un pier con su nombre · gris = muro sin pier (antepechos, dinteles, muretes) · cuadro negro = castillo

