
PLANTA BAJA — ratio de cada muro

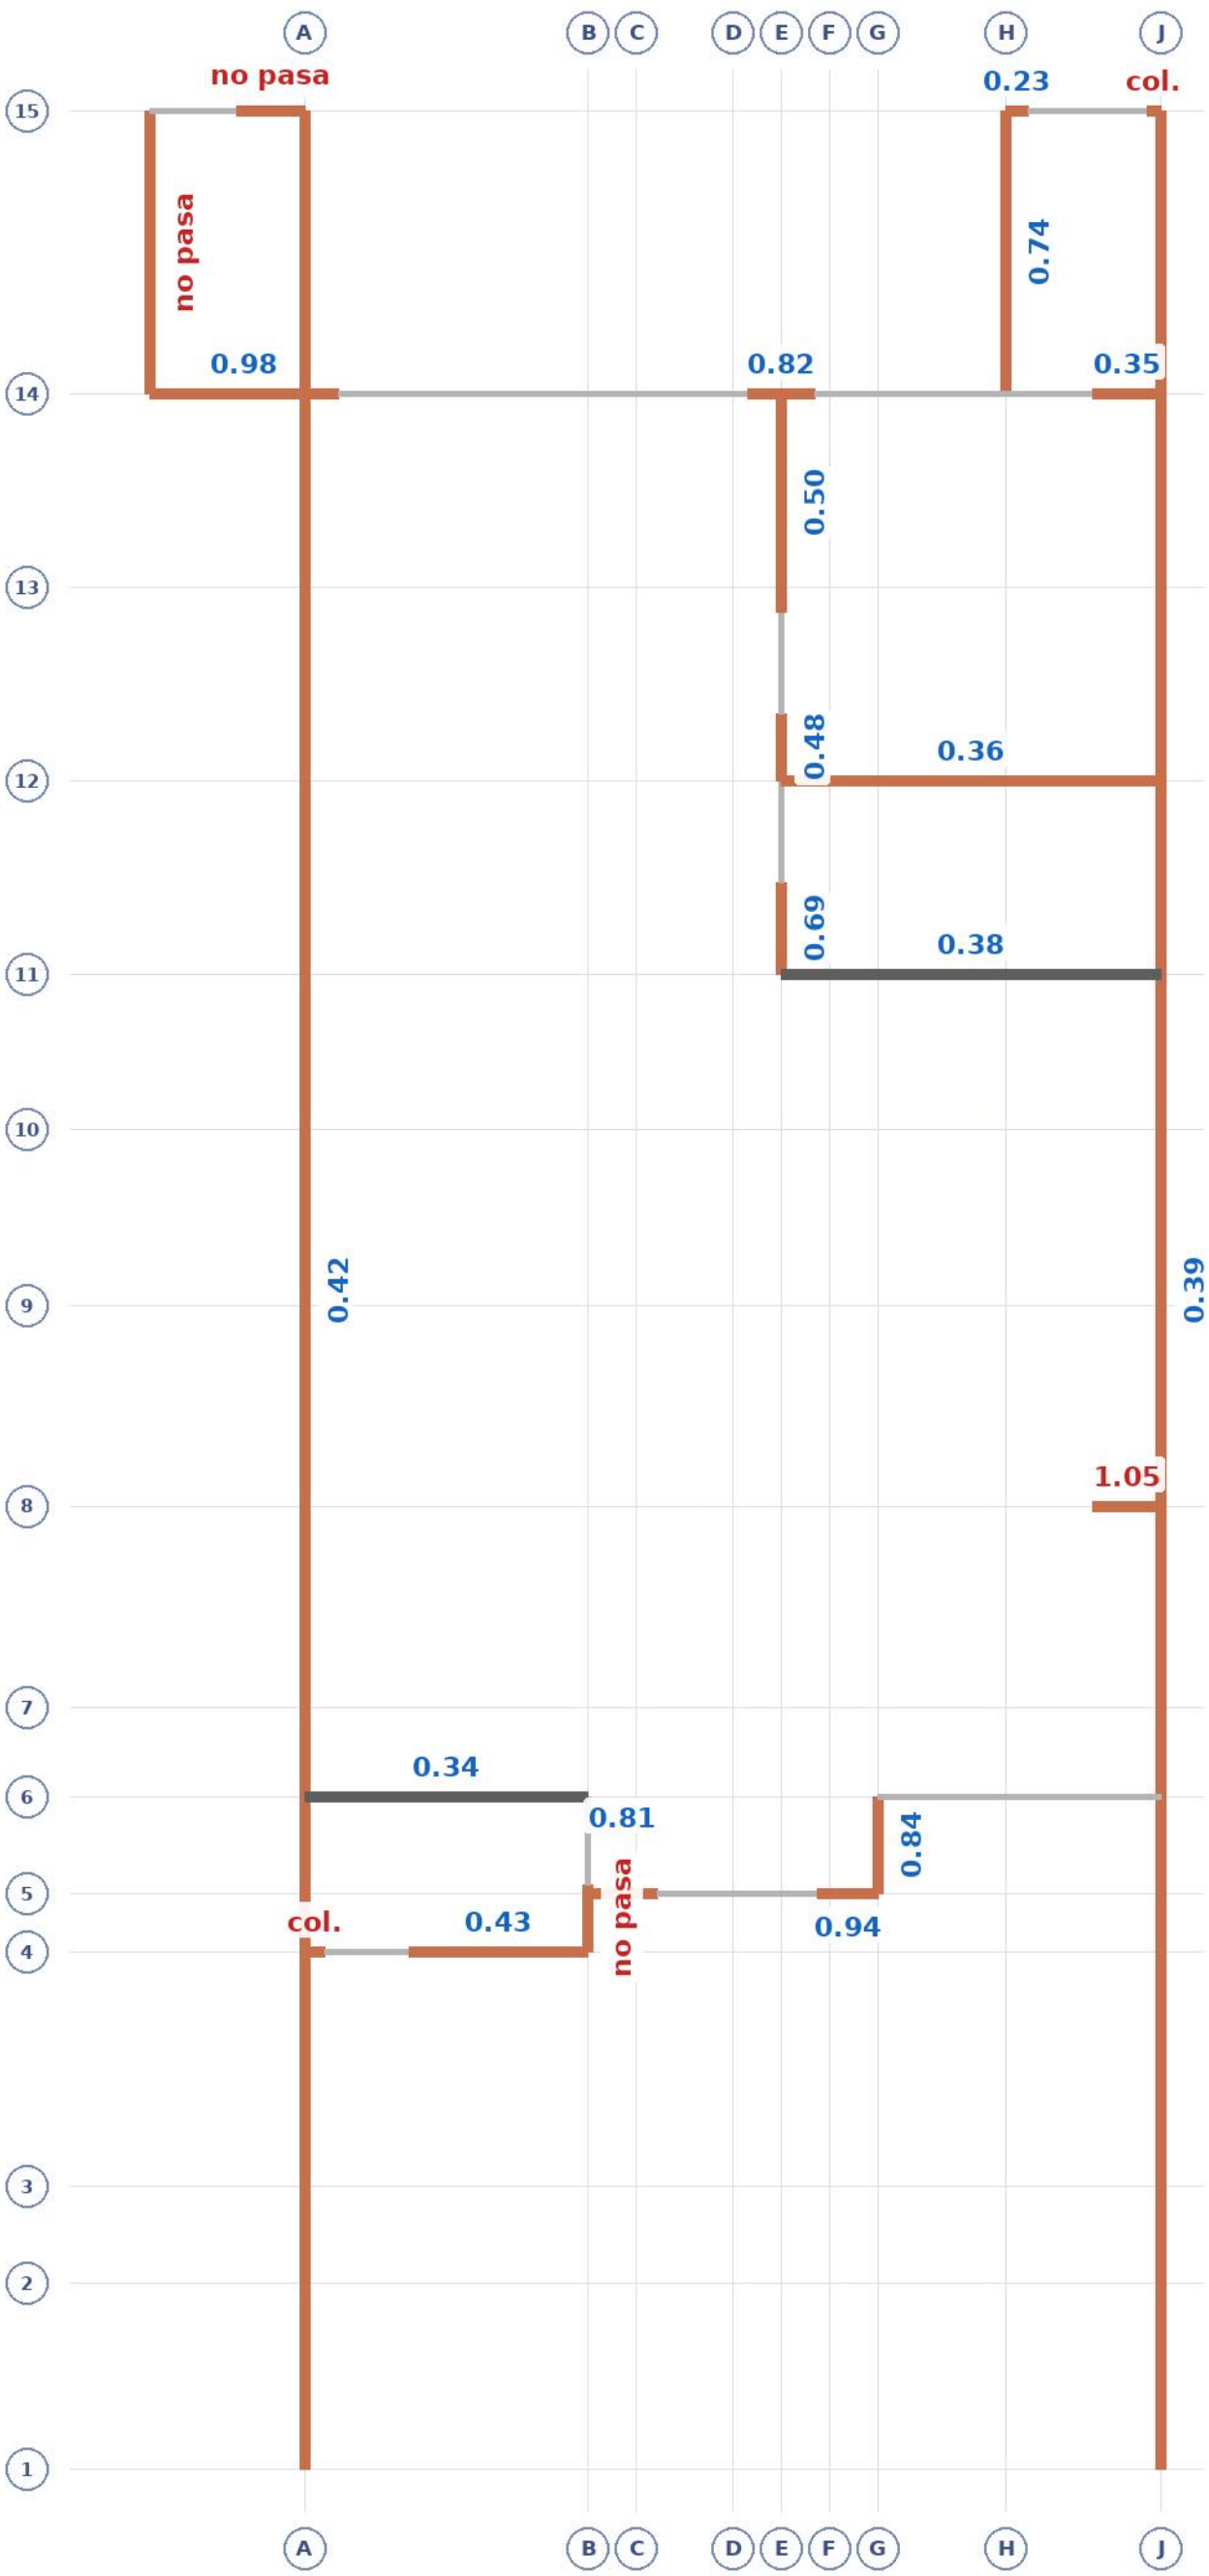

PLANTA ALTA — medida de las vigas (cm)

