
PLANTA ALTA — cómo deben quedar las vigas

medidas en cm: ancho × peralte

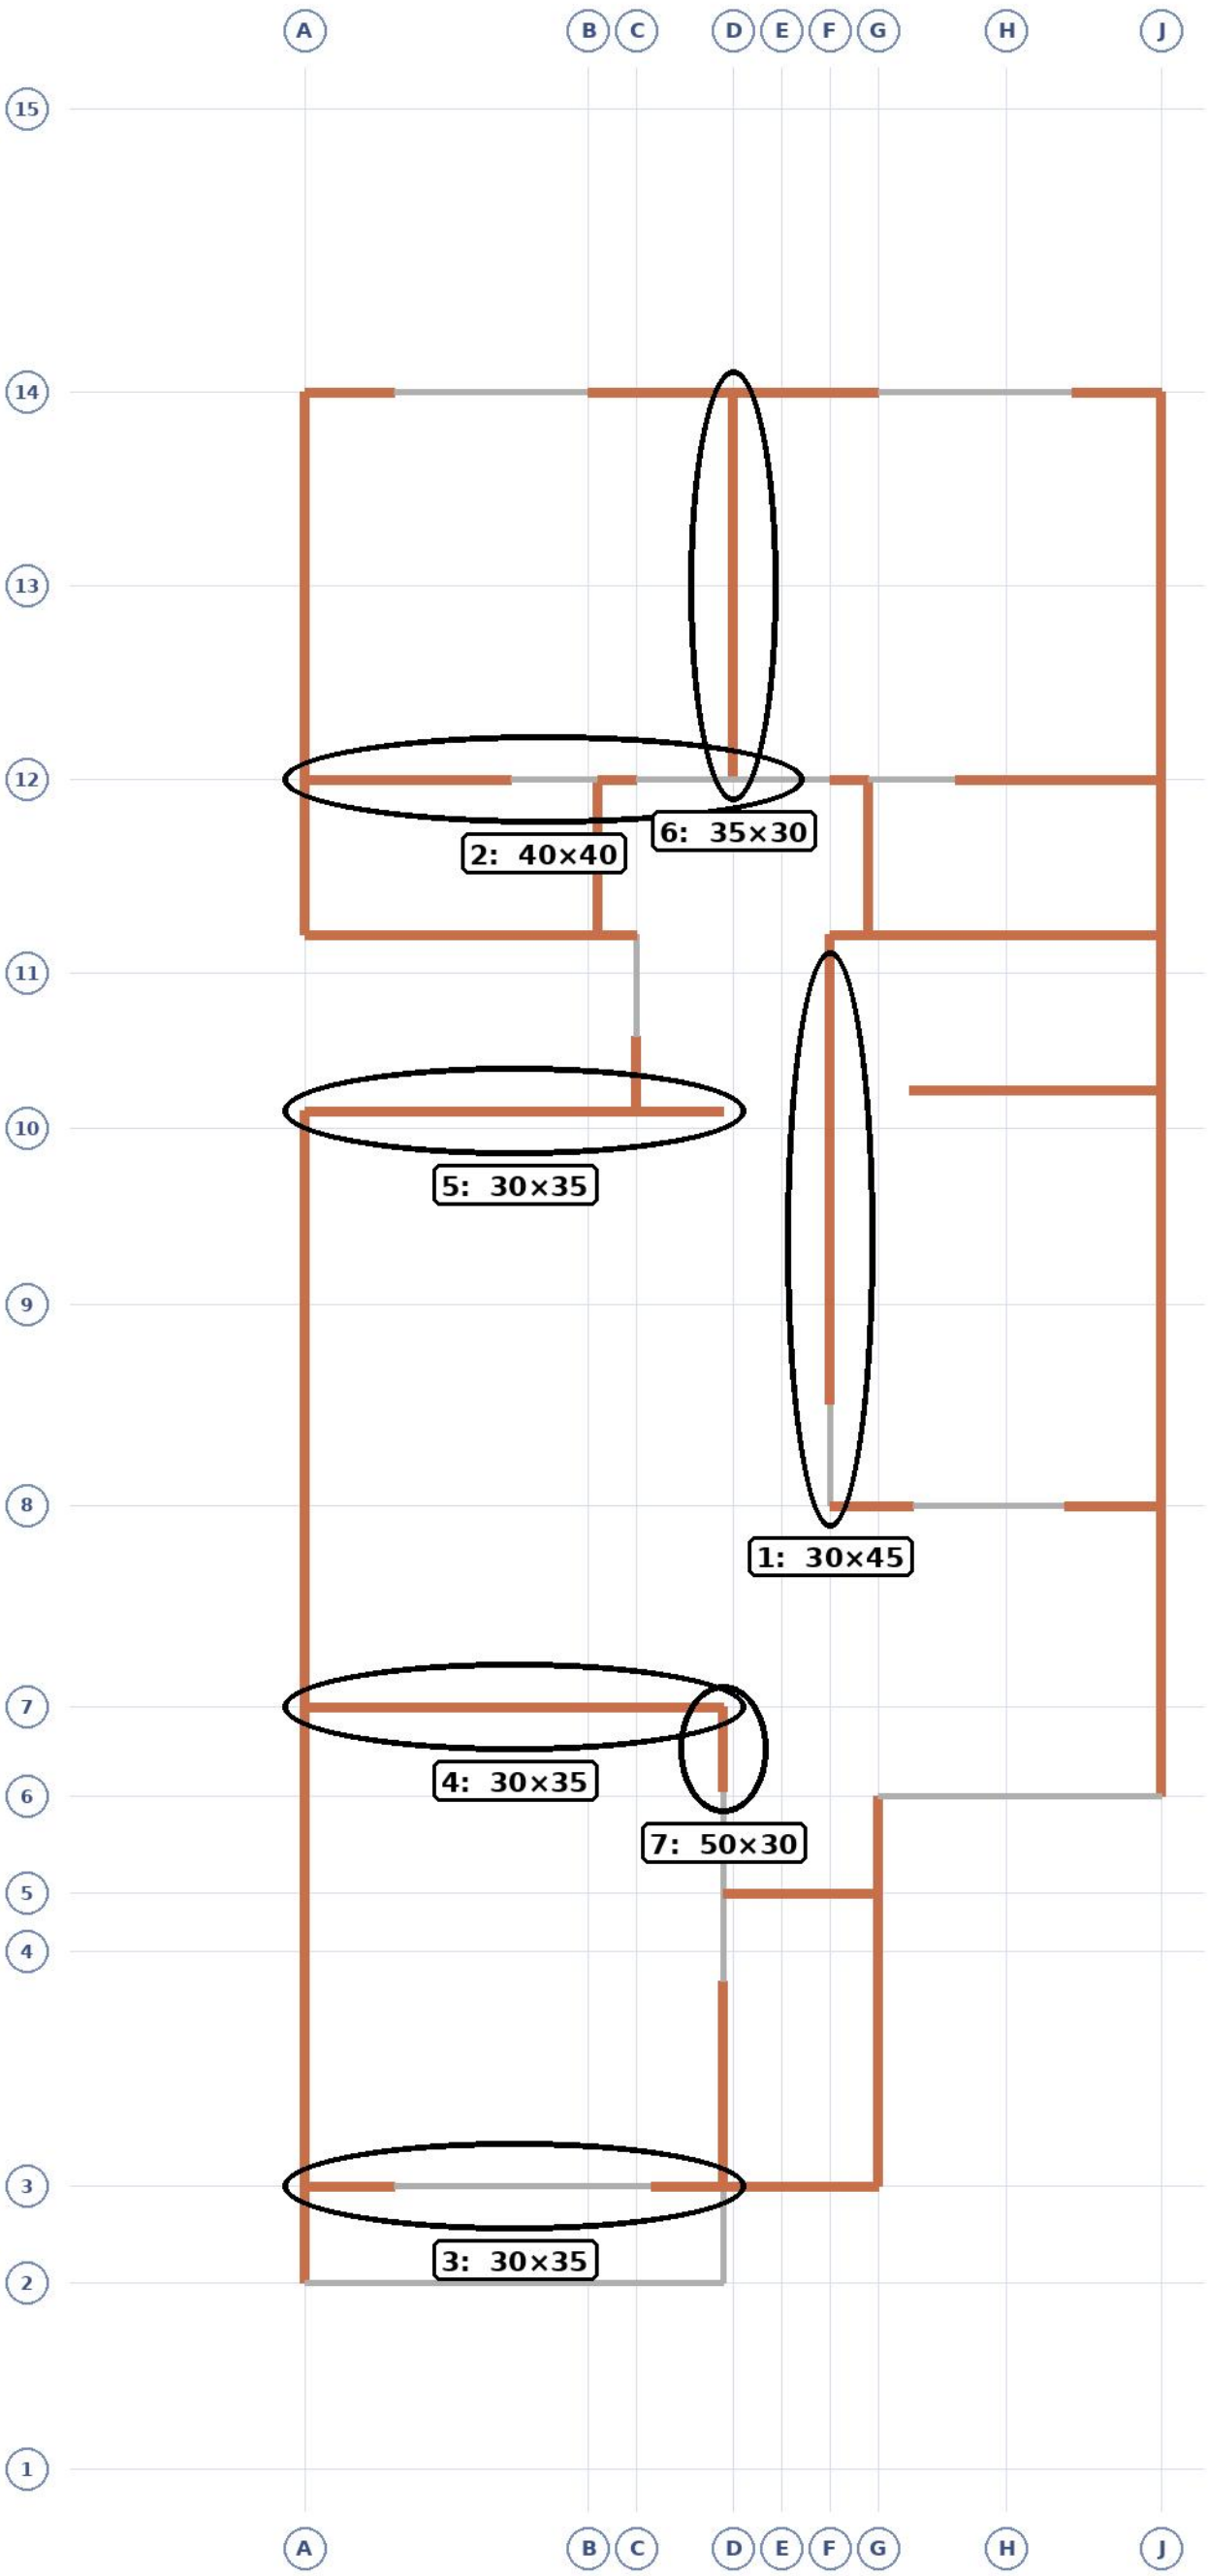

VIGAS QUE CAMBIAN

1. Eje F: **30×45**
2. Eje 12: **40×40**
3. Eje 3: **30×35**
4. Eje 7: **30×35**
5. Eje Y14.02: **30×35**
6. Eje D: **35×30**
7. Eje X4.33: **50×30**

Todas las demás: 15×30
(peralte 30 = dentro de la losa)

Las de más de 30 de peralte cuelgan abajo de la losa.

PA-3-1 (eje 3) además necesita apoyo abajo o moverlo.