
PLANTA BAJA — ratio de cada muro

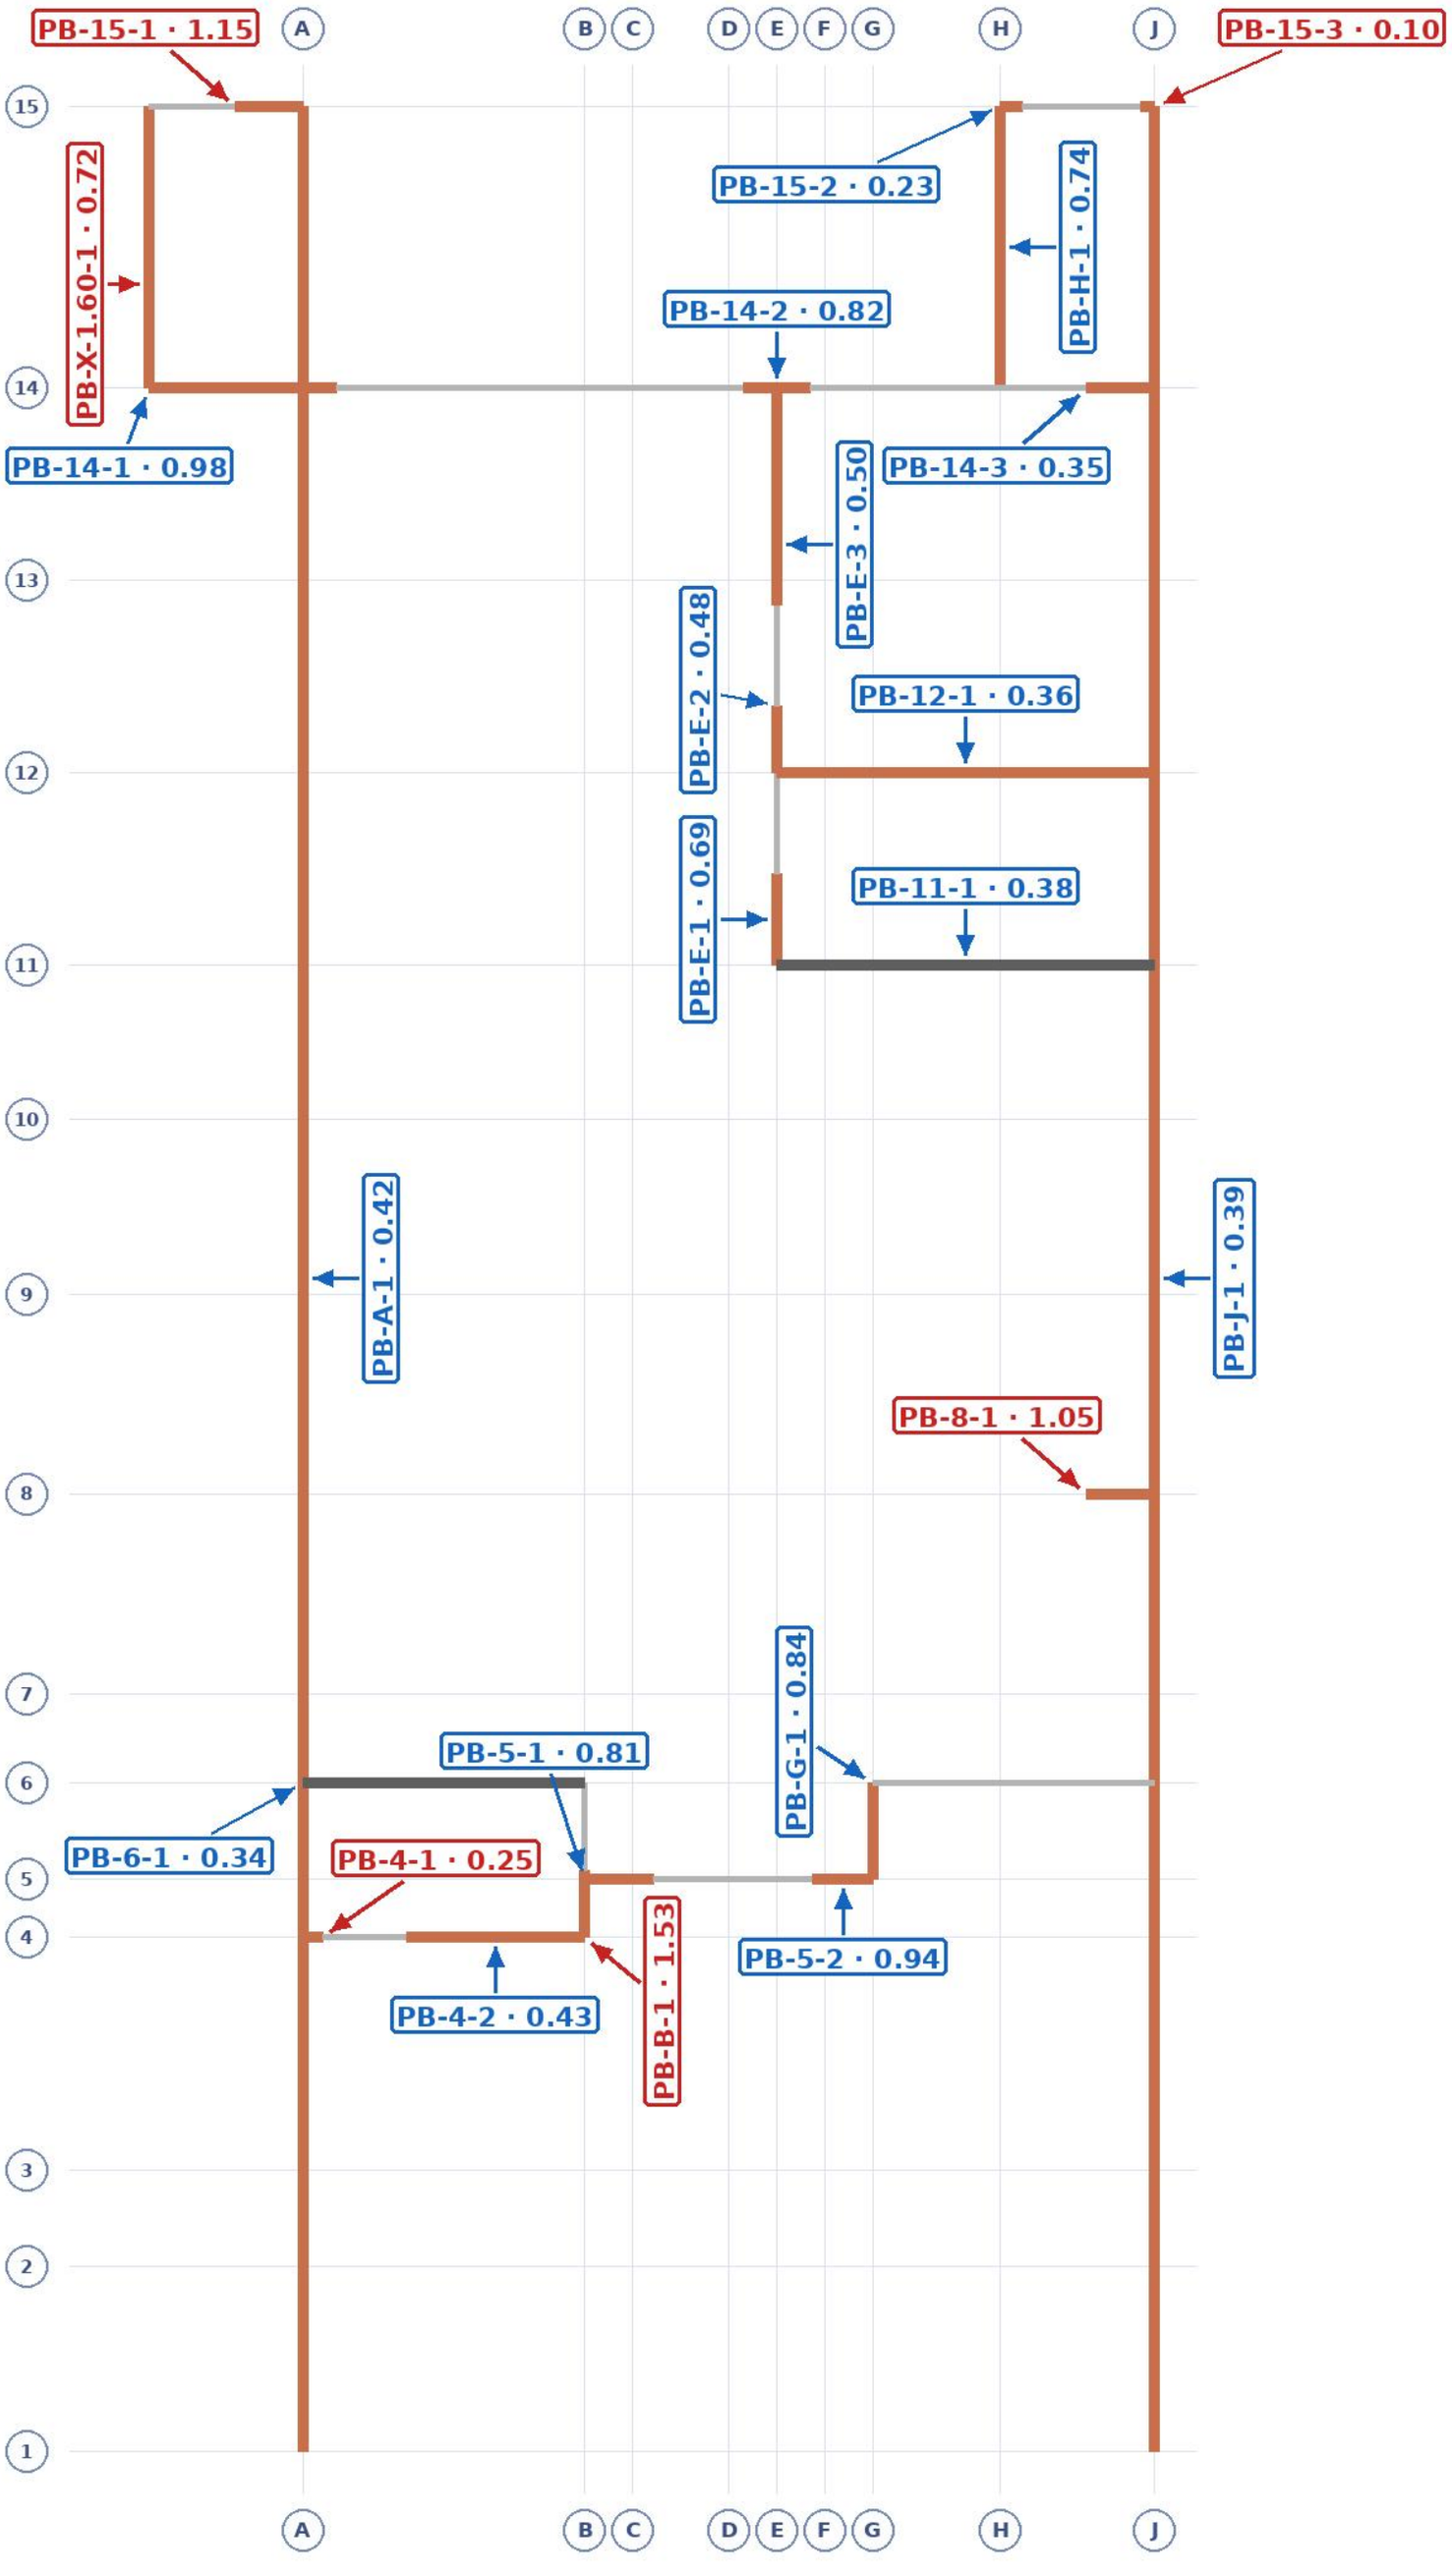

Muros sin ratio de norma

(su número es el cortante con P = 0)

Muro	Ratio	Por qué va en rojo
PB-B-1	**1.53**	Con tensión la norma no cuenta al tabique; ni con refuerzo horizontal alcanza
PB-15-1	**1.15**	Con tensión la norma no cuenta al tabique; ni con refuerzo horizontal alcanza
PB-X-1.60-1	**0.72**	Con tensión la norma no cuenta al tabique; con alambres no alcanza, va con malla
PB-4-1	**0.25**	Machón de 20 cm: va como columna
PB-15-3	**0.10**	Machón de 22 cm: va como columna

PLANTA ALTA — medida de las vigas (cm)

